


Revised ground floor plan

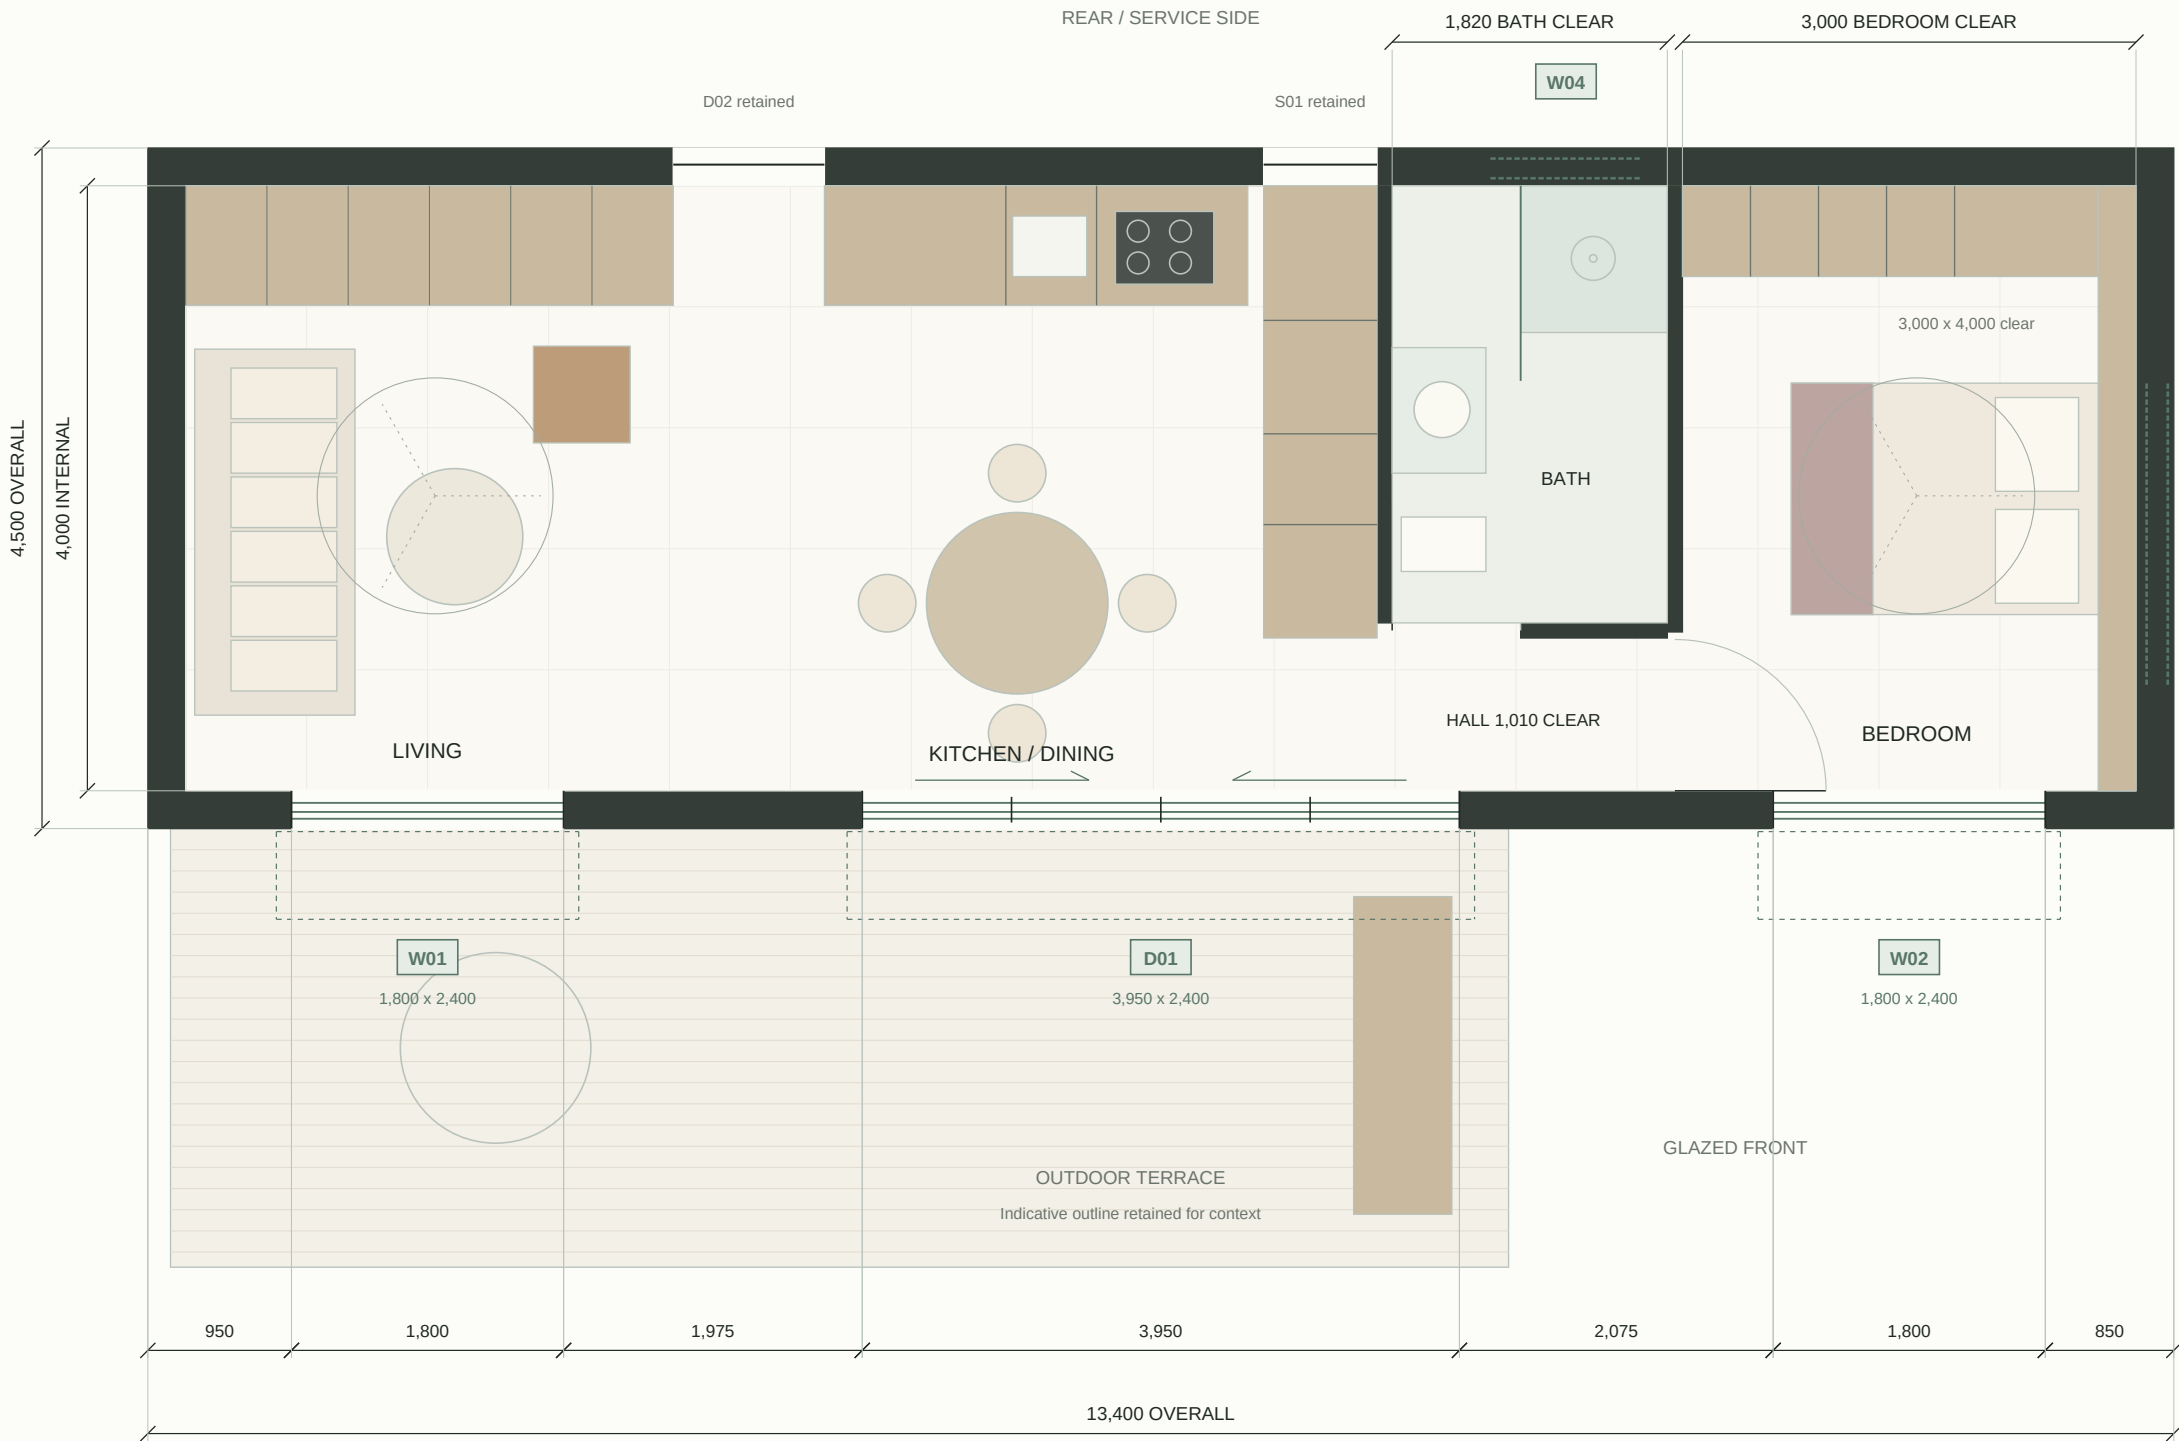

1:50 AT A3 | ALL DIMENSIONS mm | FRAME-ENVELOPE OPENING SIZES




Original architecture: Fraser & Partners. New HAAVN concept study of the window changes. Furniture indicative; footprint and principal room dimensions retained.

Window and glazing schedule

ID	Location	Width	Height	Sill	Head	Opening type	Dimension basis / status
W01	Living	1,800	2,400	0	2,400	Fixed full-height picture window	Proposed to match approved narrower facade; preceding preview width was not dimensioned.
D01	Kitchen / dining	3,950	2,400	0	2,400	Double sliding glazed doors	3950 opening retained from Fraser GA. Height, panel split and frame set-out proposed.
W02	Bedroom	1,800	2,400	0	2,400	Fixed full-height picture window	Proposed to match approved narrower facade; preceding preview width was not dimensioned.
W03	Bedroom	2,000	400	2,025	2,425	High-level window	2000 x 400 proposed from red-box proportions. 950 front-corner offset and 850 roof-top-to-head from marked elevation 2.
W04	Shower	1,000	400	2,025	2,425	High-level privacy window	1000 x 400 proposed from red-box proportions. 750 gap to service opening and 850 roof-top-to-head from marked elevation 3.


FFL = finished floor level. Sizes are overall frame envelopes, not clear glass or rough structural openings.

W01 / W02: 1,800 mm is a proposed design size to reproduce the approved narrow-window appearance. The previous render was not dimensioned, so its requested 500 mm reduction cannot be independently measured. The original GA side openings were 3,425 mm.

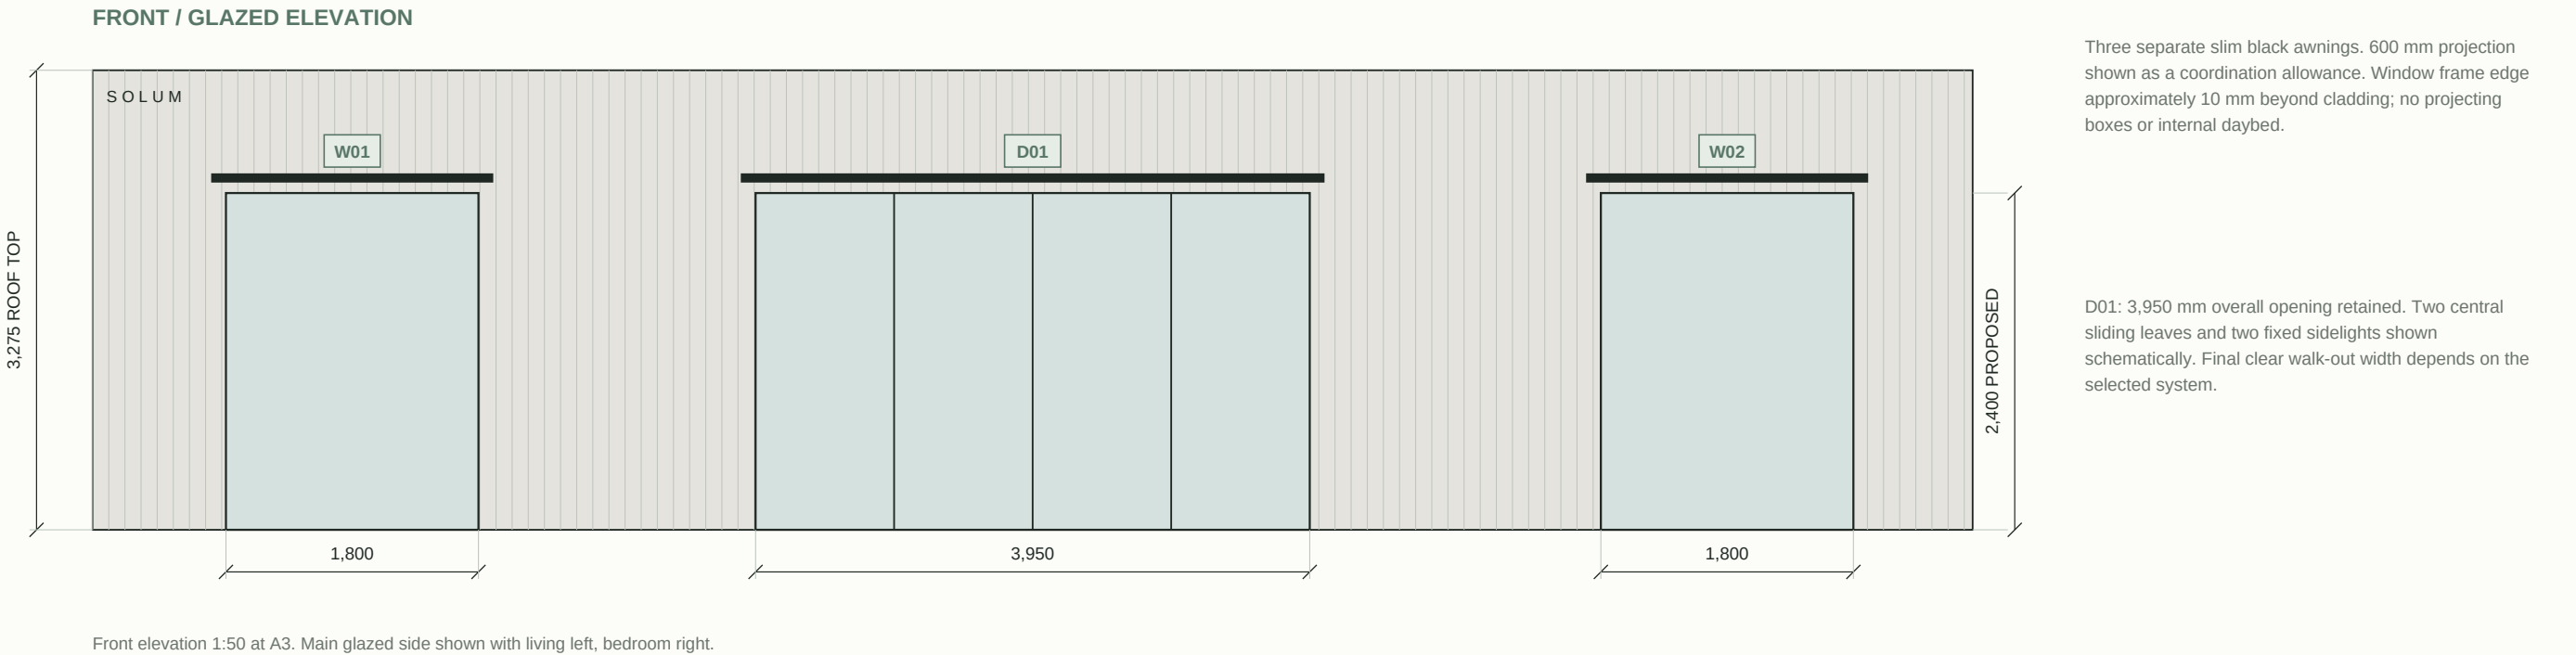


High-window elevations and setting-out

REAR / SHOWER ELEVATION

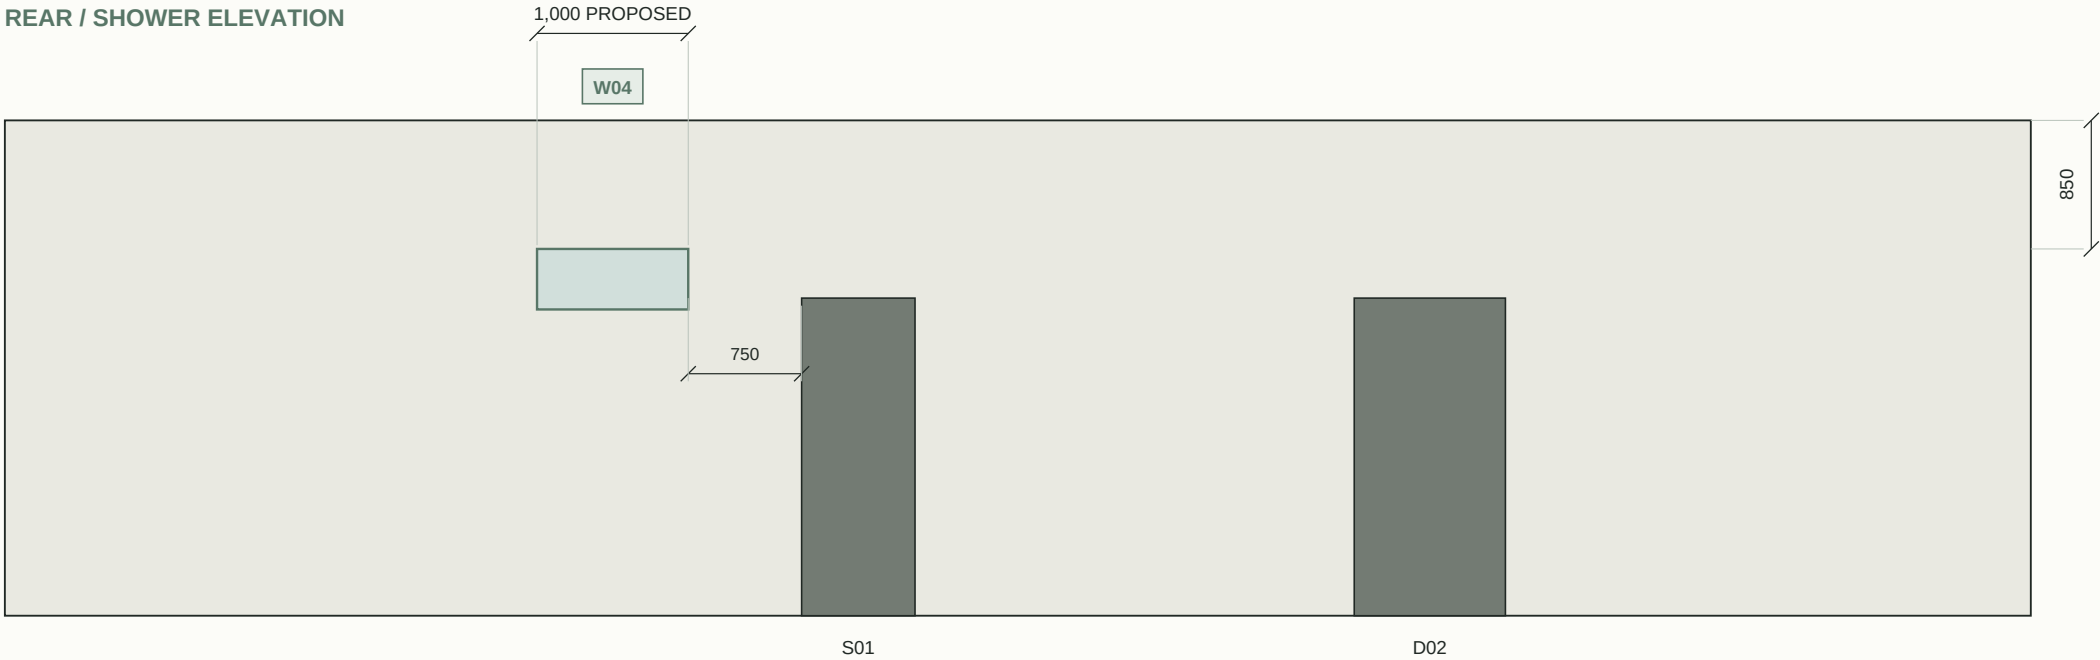

Rear entry and service access retained. No new window on the living end wall.

BEDROOM END ELEVATION

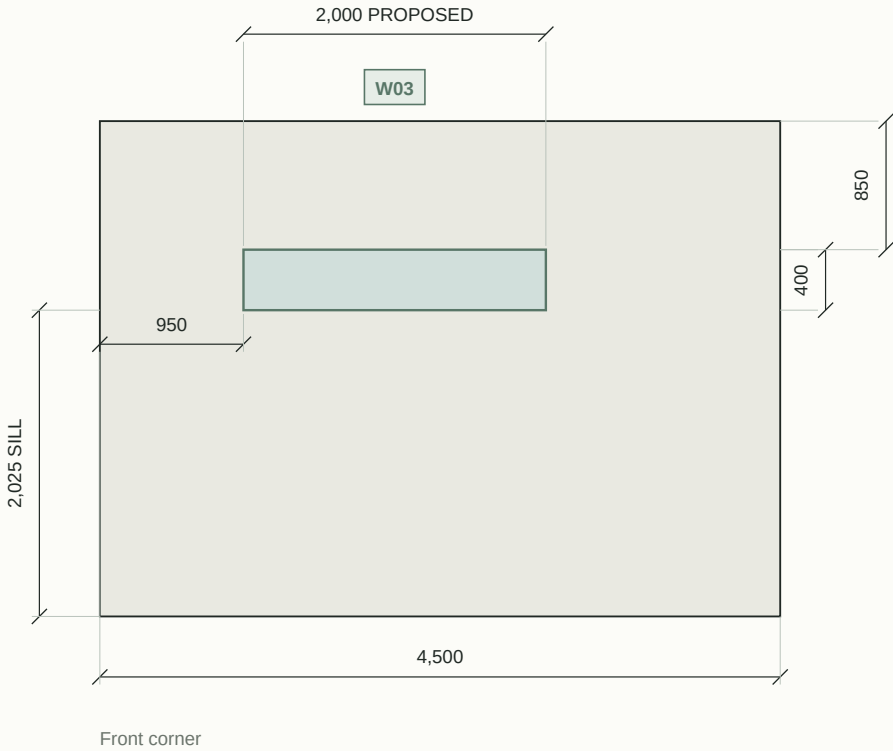

LEVEL BASIS

Fraser structural roof centre: 3,050 mm above structural floor centre.

Cladding/roof top: 350 mm above structural roof centre.

Finished floor: 125 mm above structural floor centre.

Marked roof-top-to-window-head distance: 850 mm.

Calculated high-window head above FFL: $3,050 + 350 - 125 - 850 = 2,425$ mm.

Proposed opening height: 400 mm. Sill above FFL: $2,425 - 400 = 2,025$ mm.

The red marks specify offsets, not final opening sizes. W03 and W04 widths and heights remain proposed. W03 is set 950 mm from the front corner in the bedroom end elevation. W04 is set 750 mm clear of the adjacent service opening. Final jamb clearances, framing and window operation require architect coordination.

The revised spaces in three dimensions



Modelled from the retained plan and proposed window schedule. Cream channelled sofa, matching timber joinery, stone tables, fans and the approved fixture arrangement are represented for design review. Cutaway walls are lowered for visibility; full wall and roof views are available in the interactive model.